


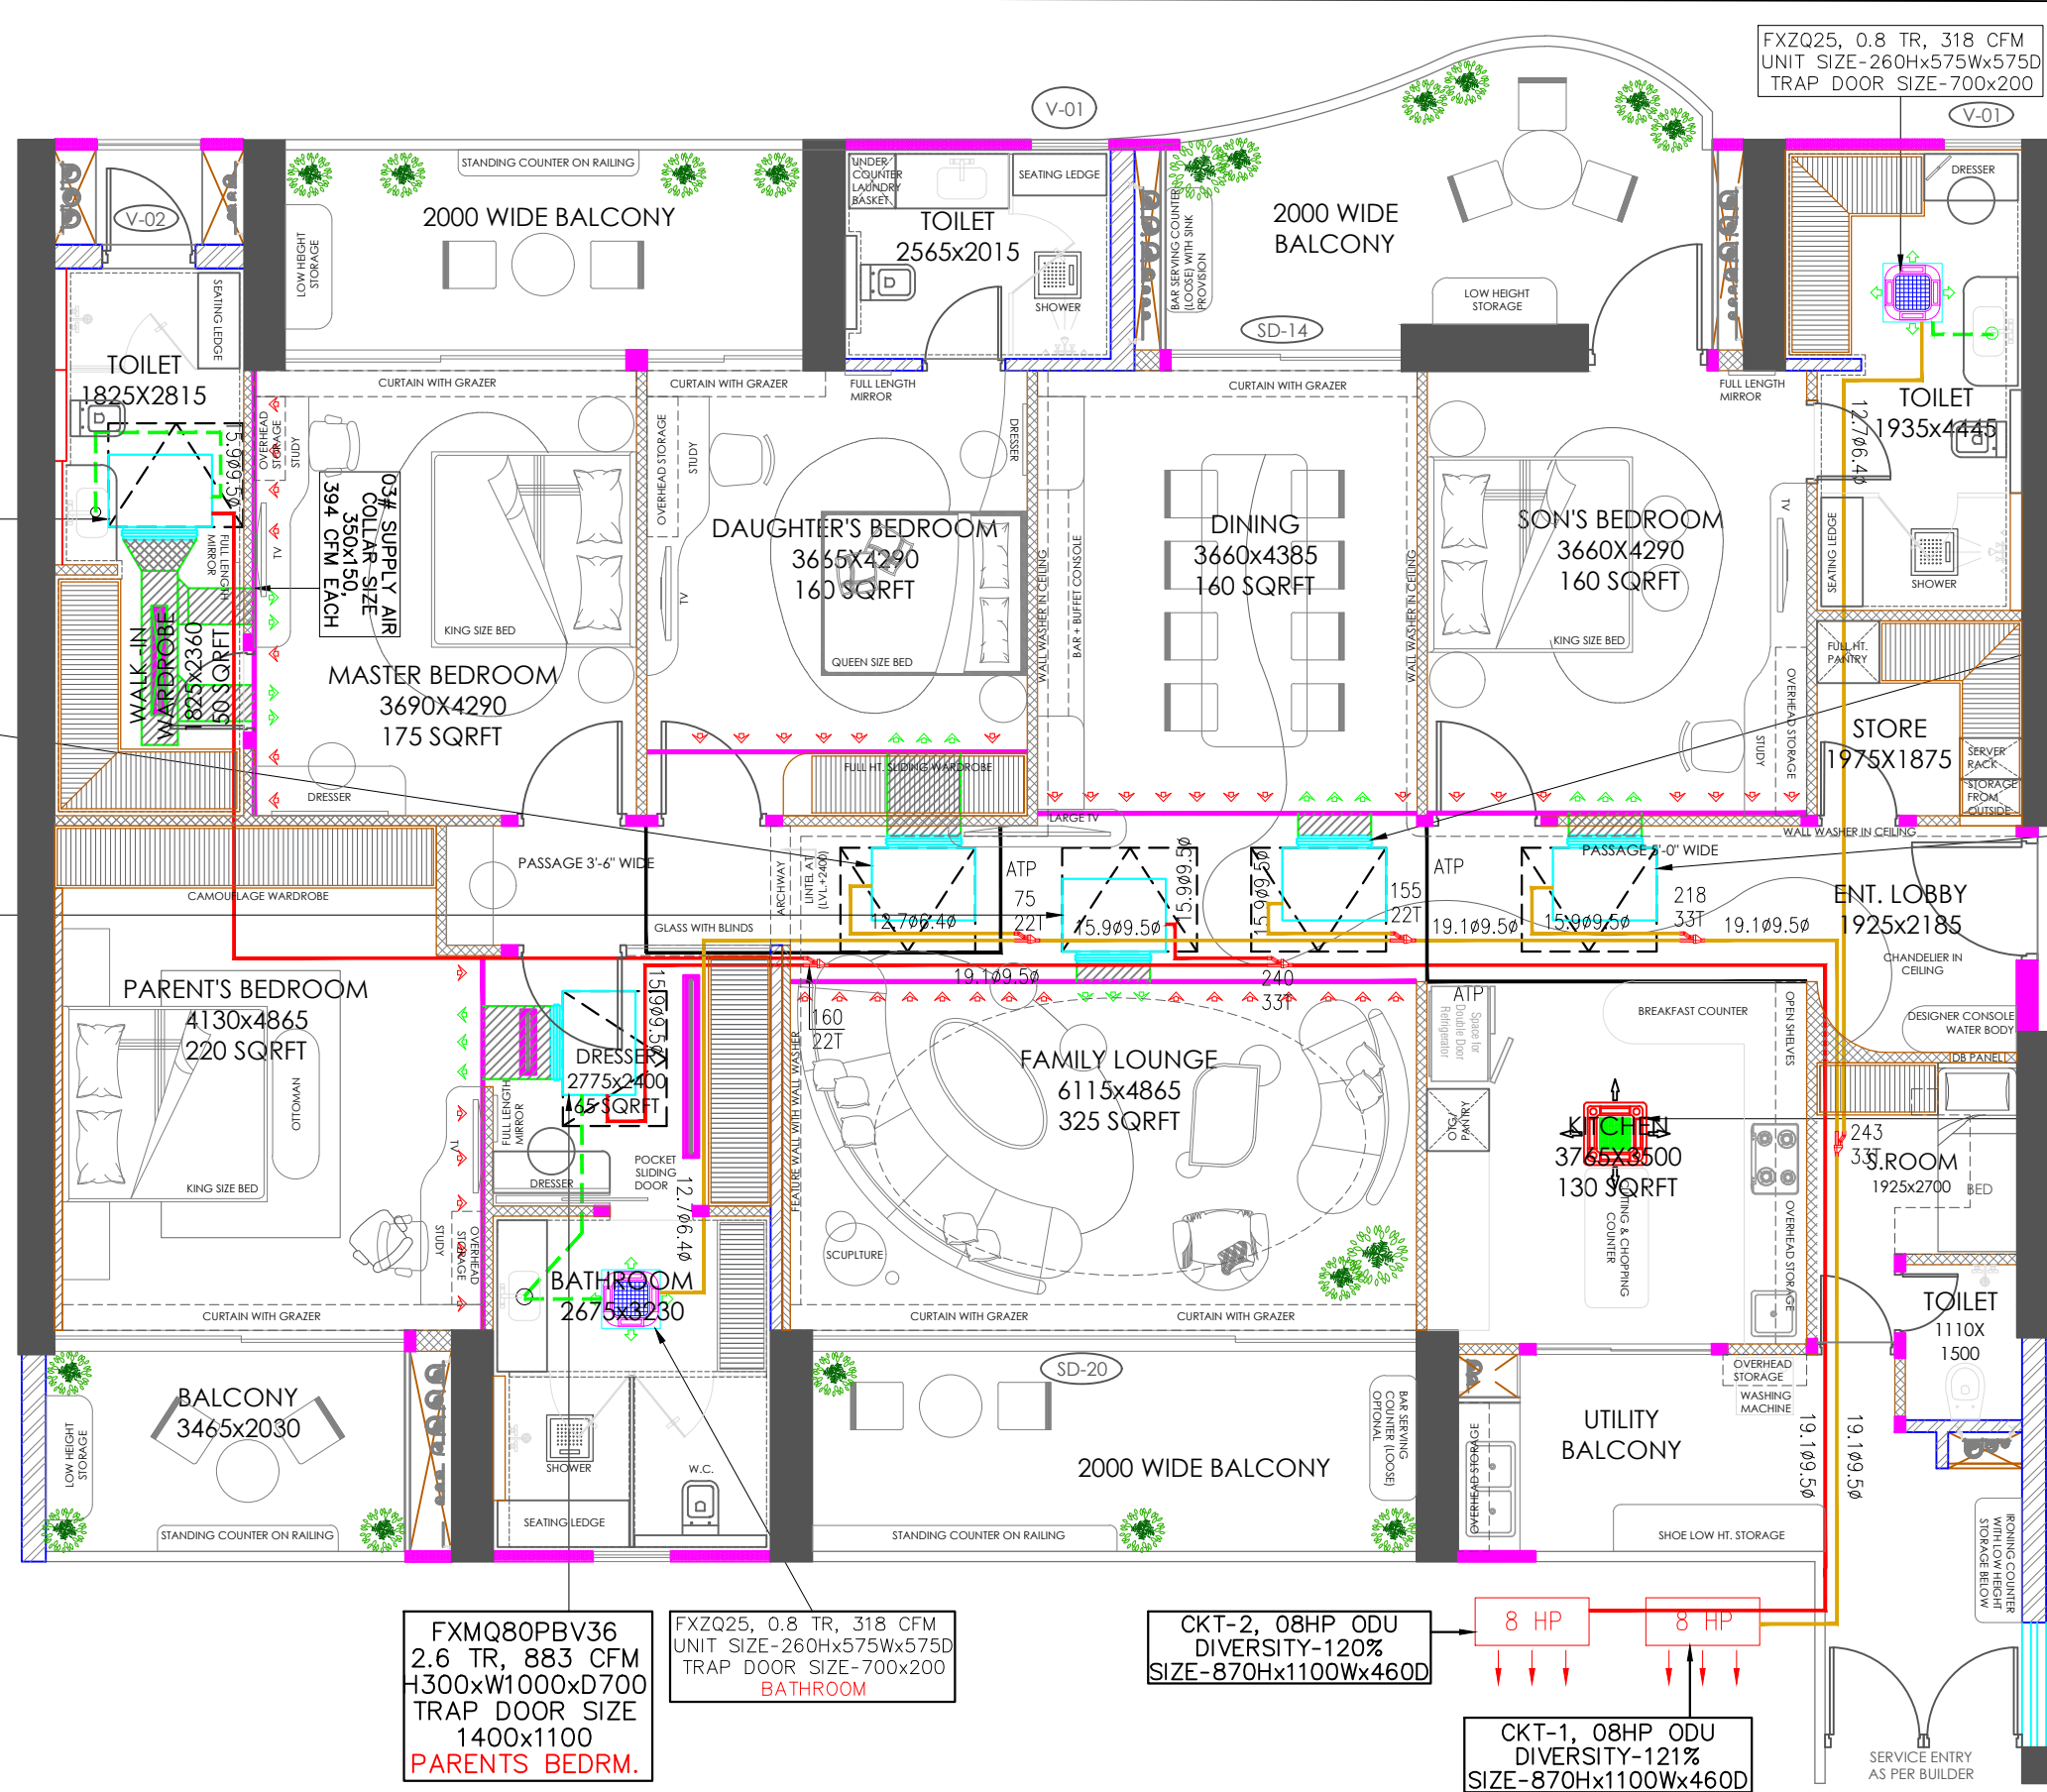

FXMQ80PBV36
2.6 TR, 883 CFM
H300xW1000xD700
TRAP DOOR SIZE
1400x1100
MASTER BEDRM.

FXMQ50PBV36
1.6 TR, 635 CFM
H300xW1000xD700
TRAP DOOR SIZE
1400x1100
DAUGHTER BEDRM.

FXMQ80PBV36
2.6 TR, 883 CFM
H300xW1000xD700
TRAP DOOR SIZE
1400x1100
FAMILY LOUNGE

FXMQ80PBV36
2.6 TR, 883 CFM
H300xW1000xD700
TRAP DOOR SIZE
1400x1100
DINING AREA

FXMQ63PBV36
2.1 TR, 688 CFM
H300xW1000xD700
TRAP DOOR SIZE
1400x1100
SON'S BEDROOM

FXMQ80PBV36
2.6 TR, 883 CFM
H300xW1000xD700
TRAP DOOR SIZE
1400x1100
PARENTS BEDRM.

FXZQ25, 0.8 TR, 318 CFM
UNIT SIZE-260Hx575Wx575D
TRAP DOOR SIZE-700x200
BATHROOM

CKT-2, 08HP ODU
DIVERSITY-120%
SIZE-870Hx1100Wx460D

CKT-1, 08HP ODU
DIVERSITY-121%
SIZE-870Hx1100Wx460D

VRV HVAC LEGEND	
	DUCTABLE INDOOR UNIT
	4 WAY CASSETTE
	1-WAY CASSETTE
	4 WAY COMPACT TYPE CASSETTE
	VRV REFF. JOINT
	VRV REFF. COPPER PIPE
	DUCT WITH INSULATION
	DUCT ACOUSTIC
	DRAIN PIPE
	OUT DOOR UNIT
	OUT DOOR UNIT POWER POINT
	INDOOR UNIT POWER POINT

NOTES

1. Drawing and dimensions are only to be read and not scaled

2. Unless otherwise mentioned, all dimensions are given in feet & inches.

3. This drawing shall be read in conjunction with relevant architectural, structural and services drawings.

4. All levels given in drawing are with reference to the Road Level as benchmarked at site

5. Any discrepancy between the architectural/ structural or services drawings must be brought to the attention of the architect by the contractor or project manager, before execution of the same.

6. All post completion construction shall be responsibility of the Owner. Architect shall not be held responsible for it.

NOTES:-

ANY BRICK WORK ON THE CANTILEVER SHOULD BE DONE IN A.A.C BLOCK

DAIKIN AIRCONDITIONING INDIA PVT LTD
210 First Floor Okhla Industrial Area Phase-III, New Delhi-110020
Tel : 011-41613868, 43834400
Website : www.daikinindia.com

DEALER PARTNER
AS AIR SYSTEMS PVT. LTD.
DSIC INDUSTRIAL SHED-65
OKHLA INDUSTRIAL ESTATE PHASE-1
E-mail : engg@asairsystems.co.in
Telefax 40589773 New Delhi 110020

SITE ORIENTATION :-

CLIENT :- Mr. Dipesh Batheja
CONCEPT BY :- Ar. Osama Aijaz
CKD BY :- Ar. Piyush Mittal

DRAWING TITLE :- LAYOUT PLAN
DRG. NO. AD-01

DATE :- 02/06/2026
PROJECT :- B2/811, AMARYLLIS, NEW DELHI

DRAWING DETAIL

Tower	B2-811
DRAWING BY	Mr. Kausar Ali
CHECKED BY	Mr. Syed Meraj
Drawing	HVAC SHOP DRAWING
DATE - 02.06.2026	REV-02

B 2/811 AMARYLLIS